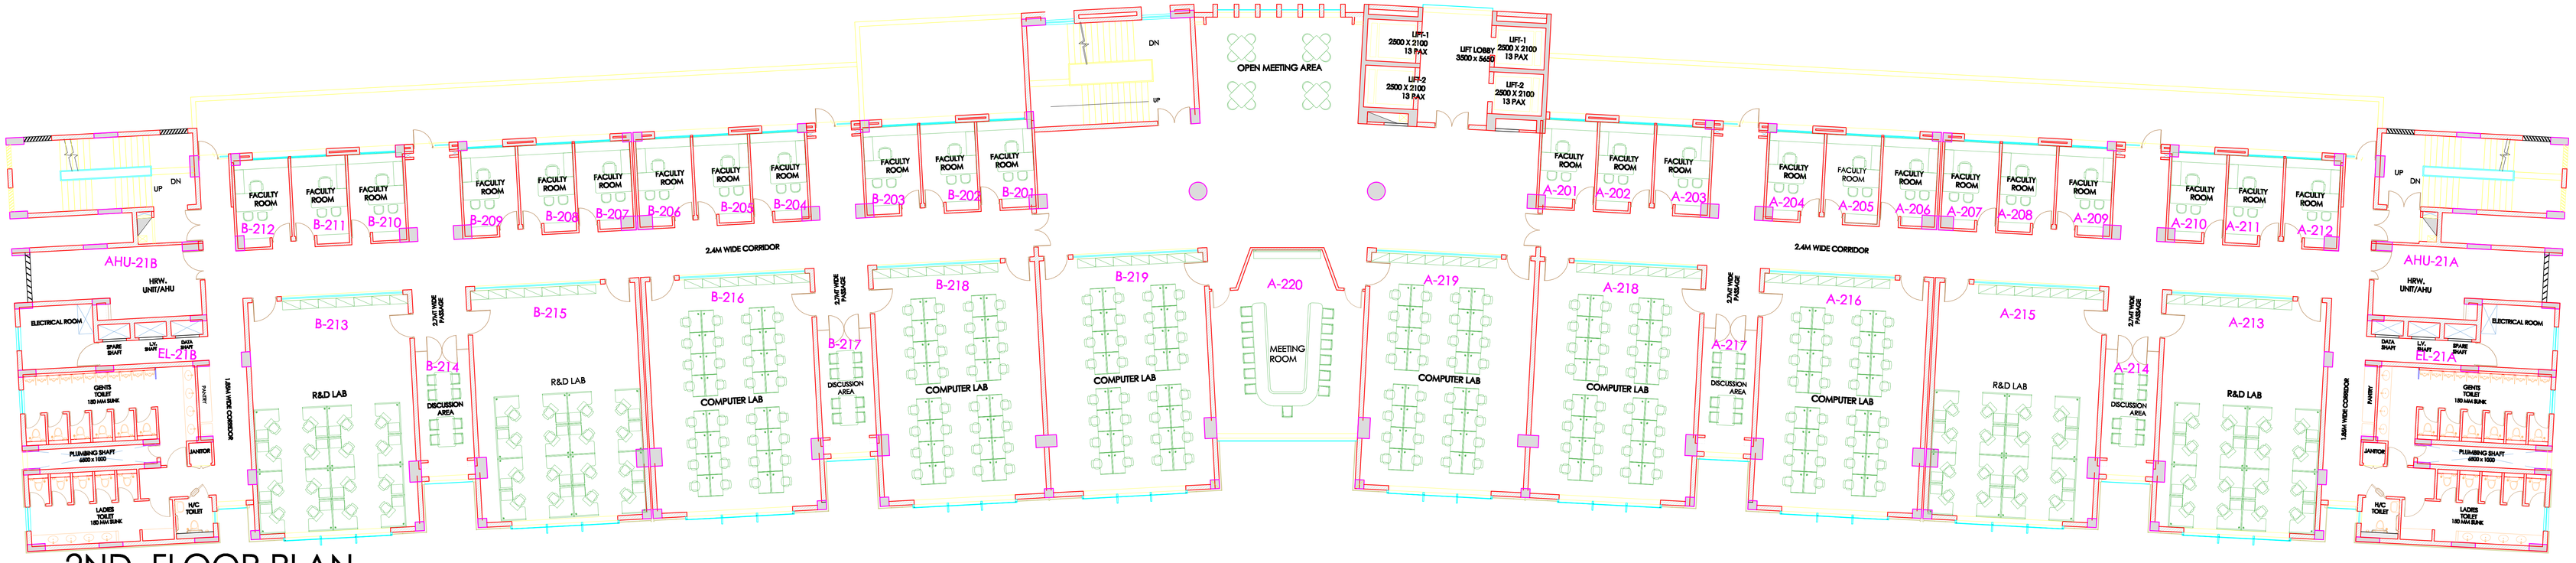


2ND FLOOR PLAN

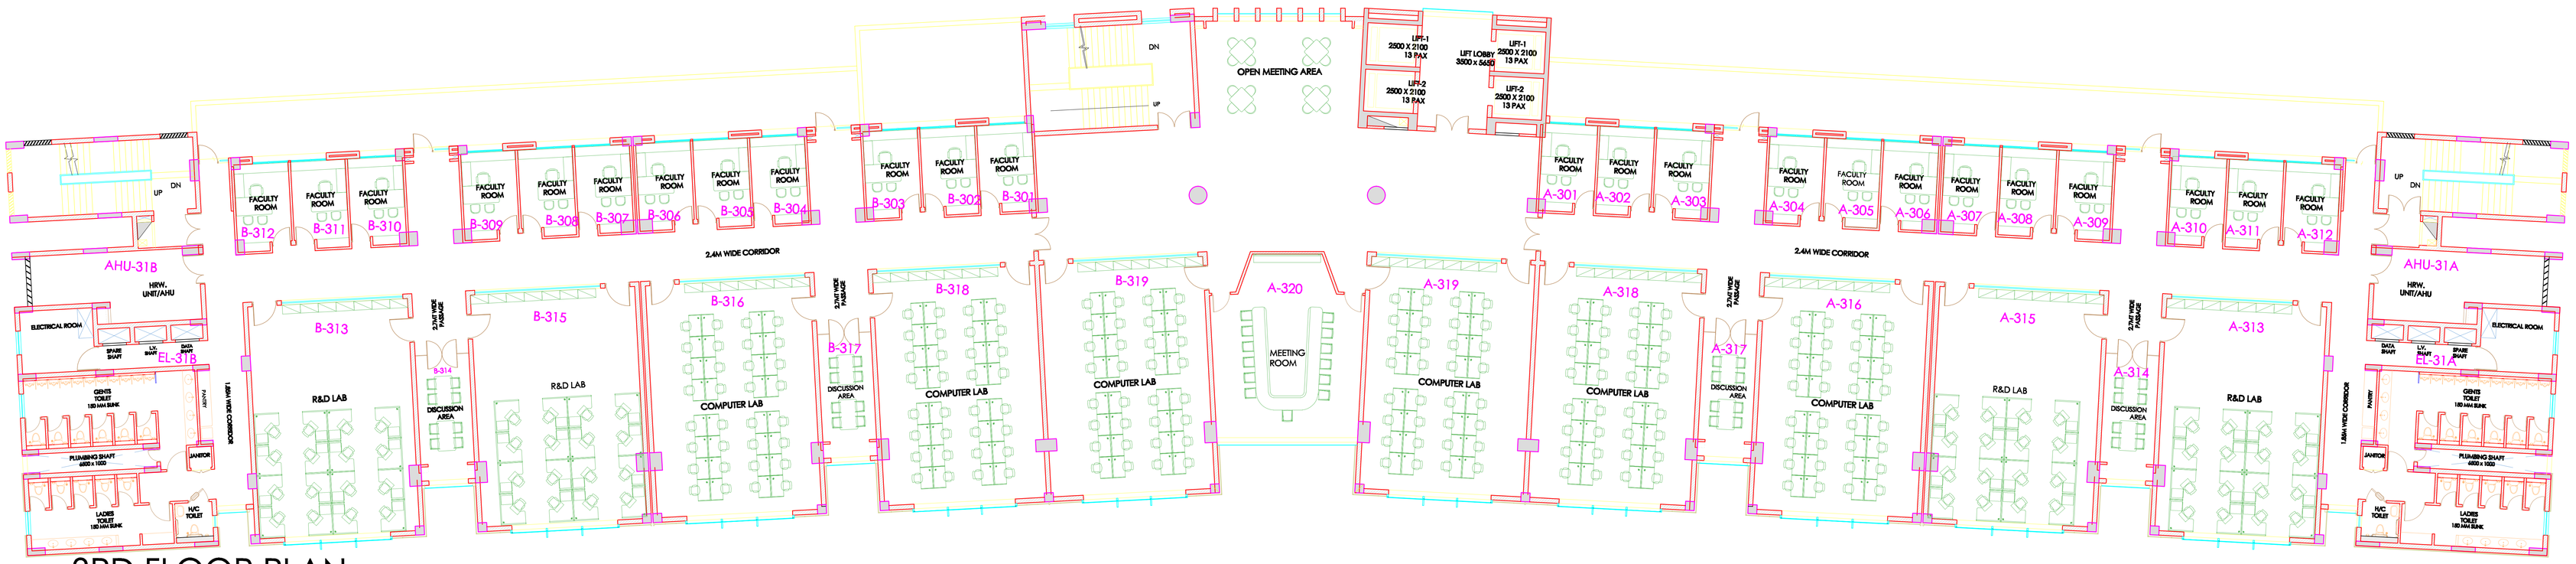


3RD FLOOR PLAN